




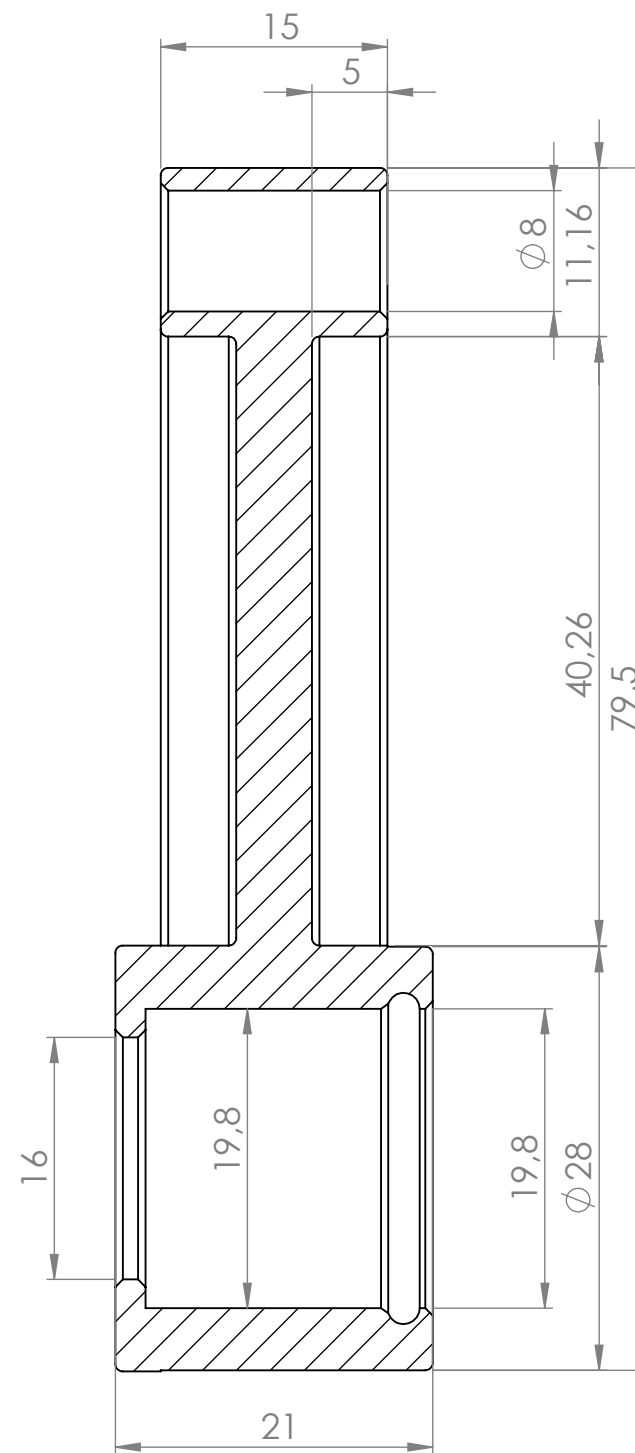

SECCIÓN A-A
ESCALA 2 : 1

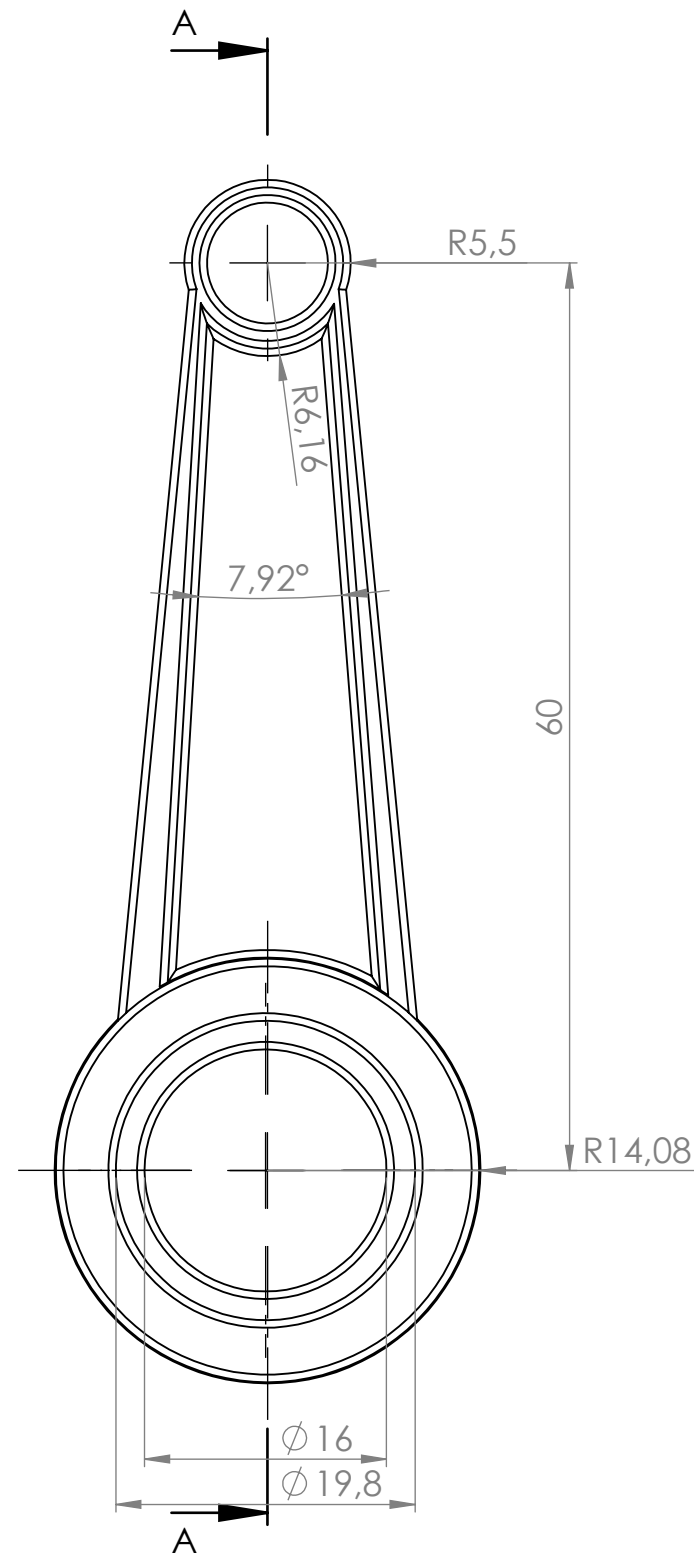

Nota:
 -Tol.Gral.S/N ISO 2768-mk
 -Chaflandes no acotados 0.3x45
 -Radios no acotados R0.3
 -Acabados superficiales no especificados H7

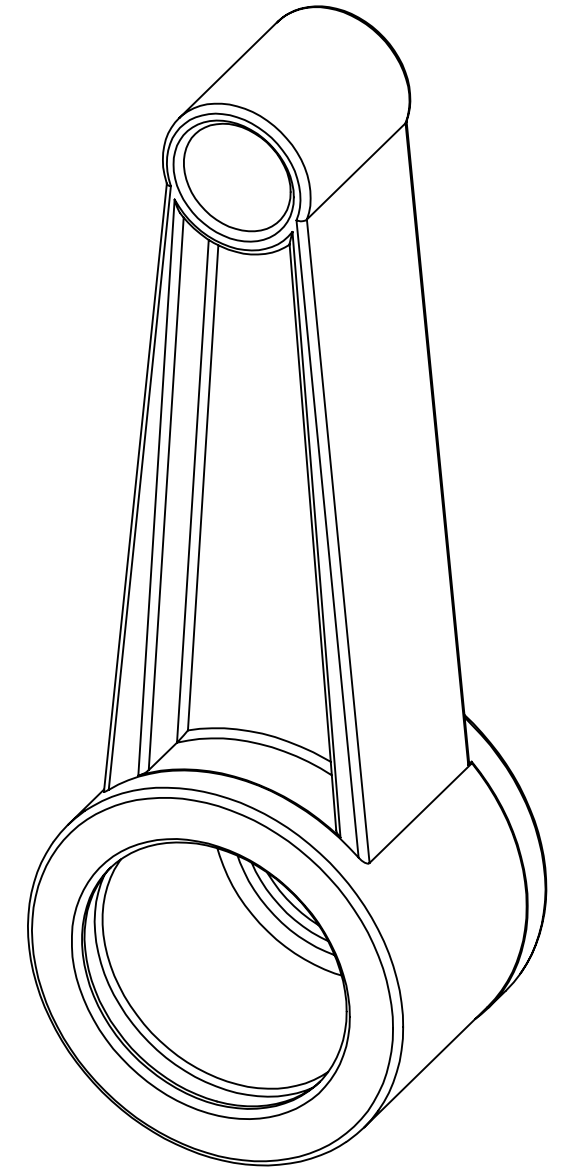

Pes [g] 12.33	Volum [cm³] 12.33	Material Material <sin especificar>		Acabat					
 ISO-E	DATA	COGNOMS, NOM	Assignatura DIRT	Grup D4521	Projecte Bomba de Succio				
DIBUIXAT	09/04/2025	Spiluttini Lukka	Denominació Biela						
PROFESSOR	Espin Agüera Daniel								
 UNIVERSITAT POLITÈCNICA DE CATALUNYA BARCELONATECH		Document PlanoBiela			Codi P1-006				
Escola Politècnica Superior d'Enginyeria de Vilanova i la Geltrú		 <table><tr><td>Format A3</td><td>Escala 1:1</td><td>Pàgina 1/1</td><td>Revisió</td></tr></table>				Format A3	Escala 1:1	Pàgina 1/1	Revisió
Format A3	Escala 1:1	Pàgina 1/1	Revisió						
Escola Politècnica Superior d'Enginyeria de Vilanova i la Geltrú EPSEVG Av. Víctor Balaguer, 1 08800 Vilanova i la Geltrú Tel.: 93 896 77 01 https://www.epsevg.upc.edu									