


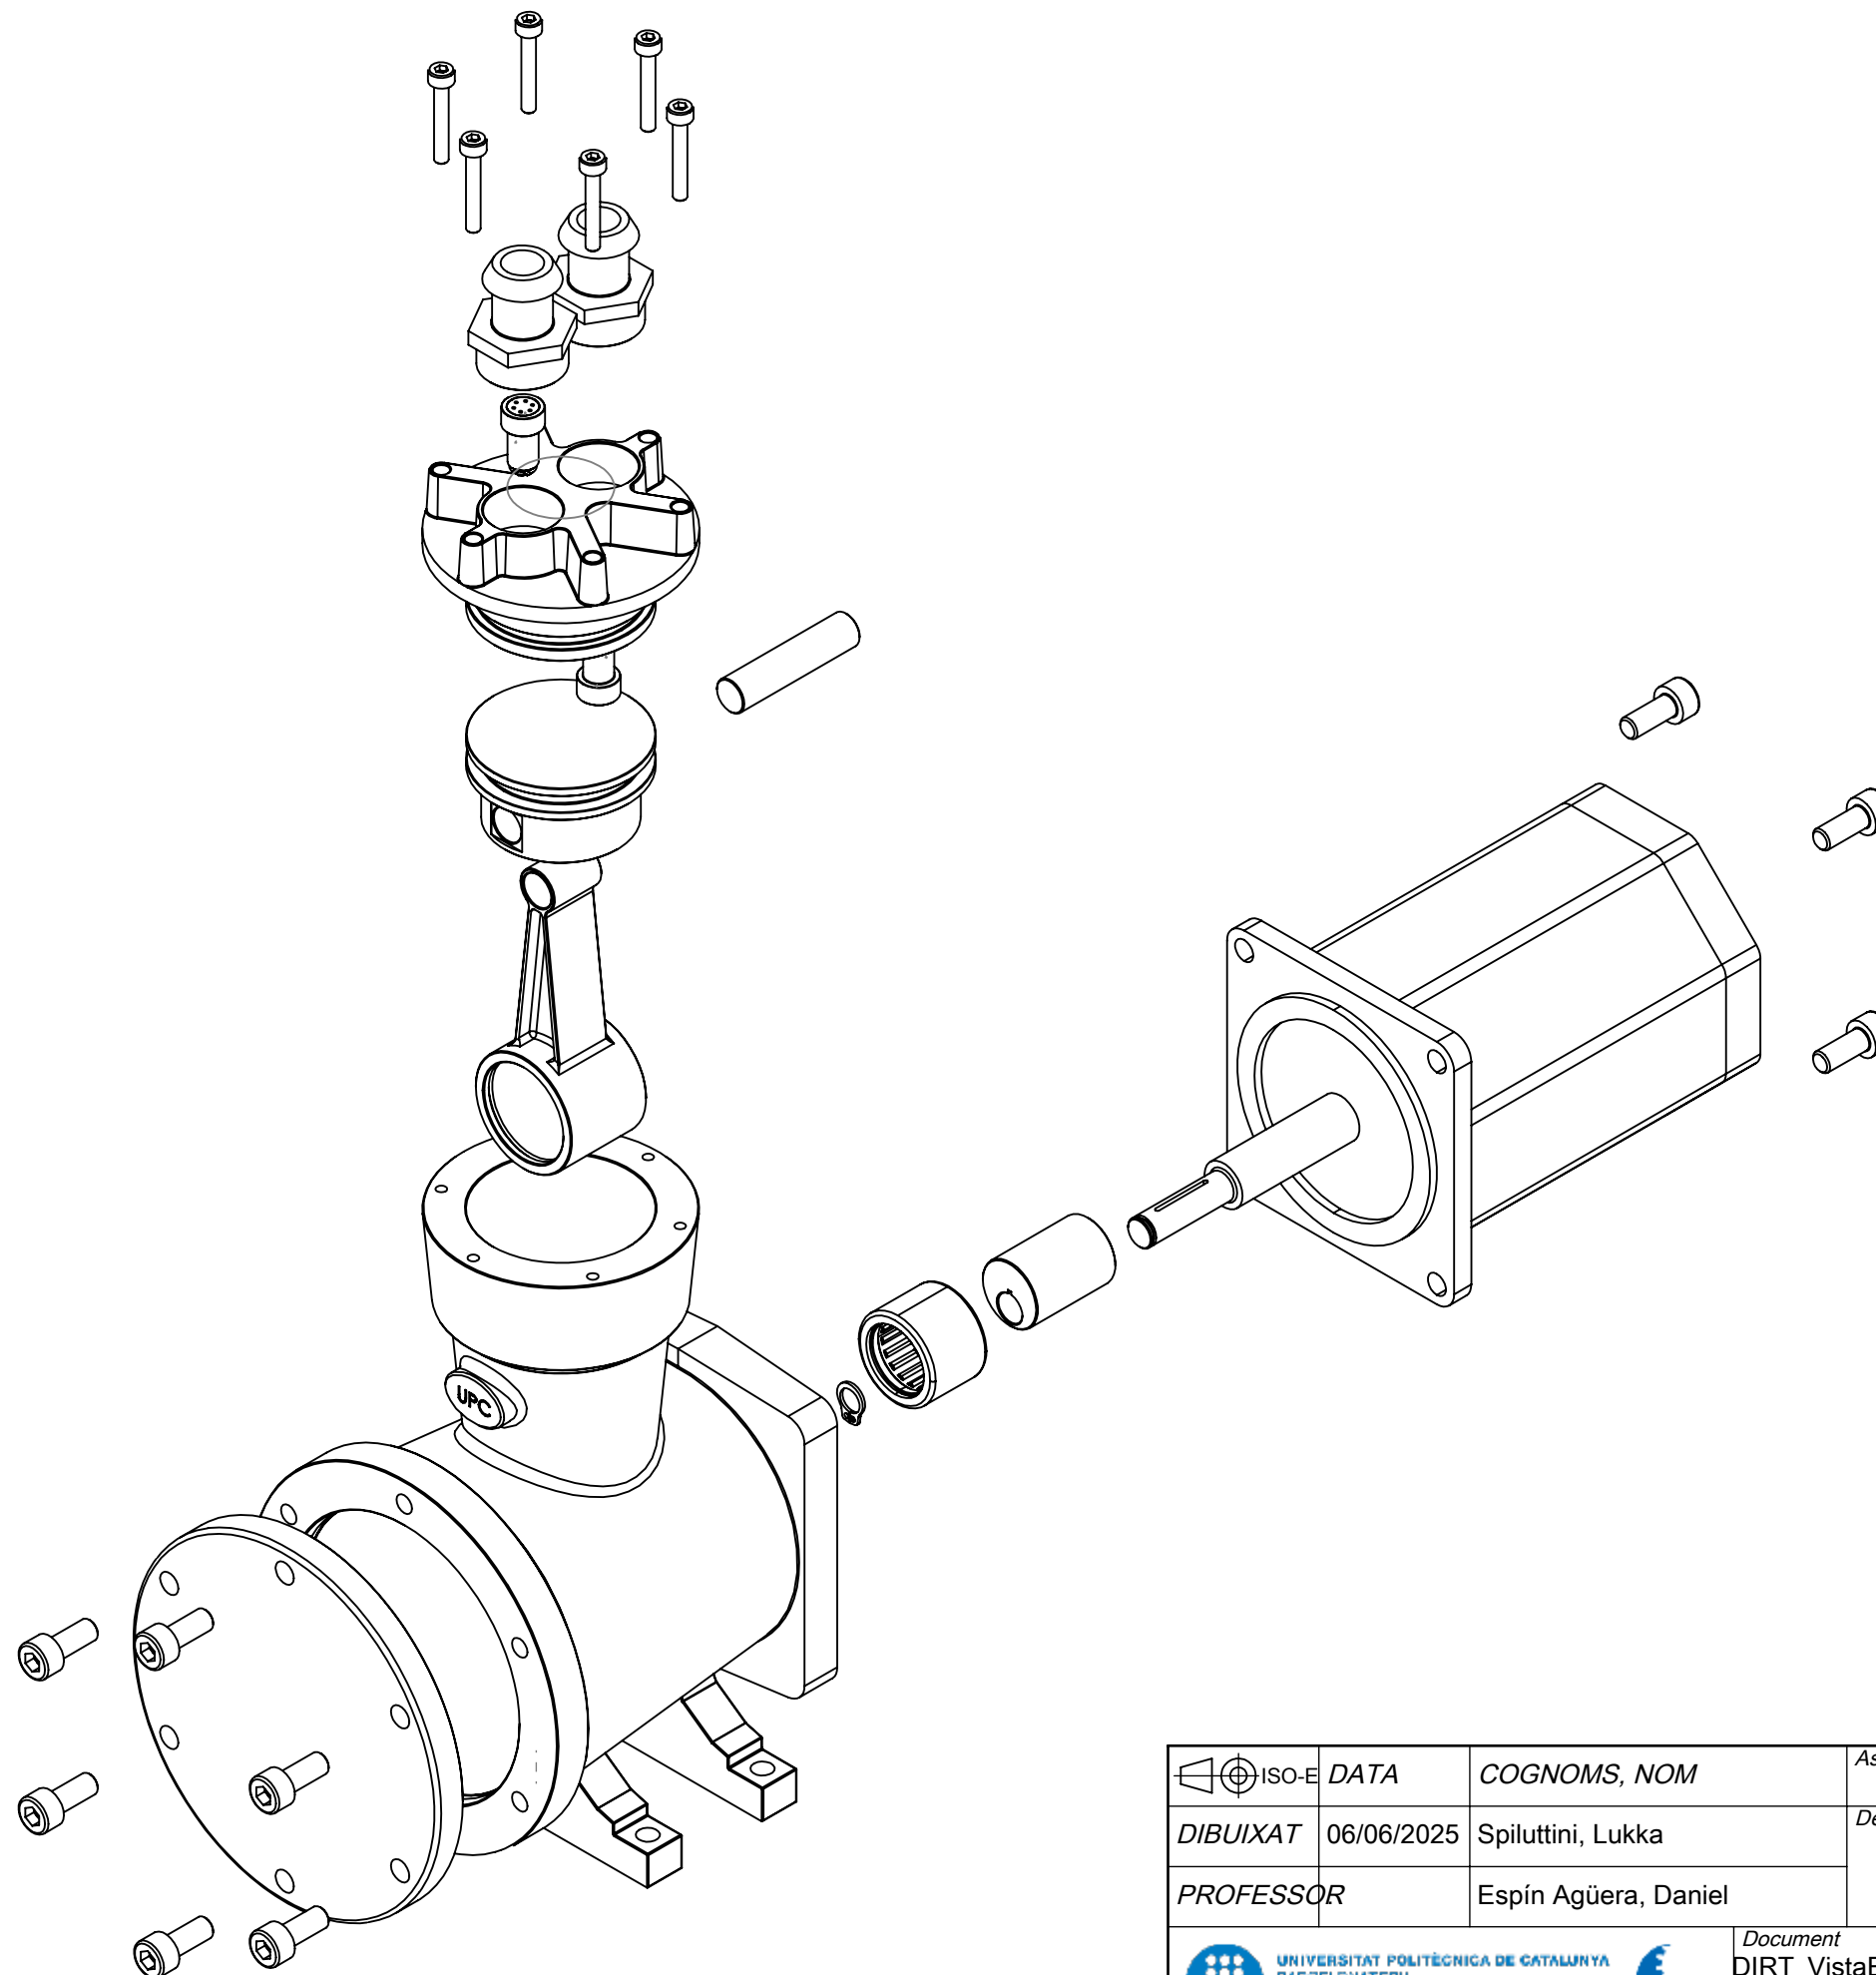

 ISO-E	DATA	COGNOMS, NOM	Assignatura DIRT	Grup D4521	Projecte Bomba de Succió
DIBUIXAT	06/06/2025	Spiluttini, Lukka	Vista Explosionada		
PROFESSOR		Espín Agüera, Daniel			
 UNIVERSITAT POLITÈCNICA DE CATALUNYA BARCELONATECH Escola Politècnica Superior d'Enginyeria de Vilanova i la Geltrú			Document DIRT_VistaExplosionada_Y6049563W	Codi P5-001.2	
 EPSEVG			Format A3	Escala 1:5	Pàgina 1/1
Escola Politècnica Superior d'Enginyeria de Vilanova i la Geltrú Av. Victor Balaguer, 1 08800 Vilanova i la Geltrú Tel.: 93 896 77 01 https://www.epsevg.upc.edu					